


GREENEYE NURSERY — MS STRUCTURE: SYMMETRIC COLUMN GRID

6 columns | 100×100 SHS | ISMB 150 beams | Composite deck slab | Symmetric grid: N1-W1-SW (West) + N2-NE-SE (East)
Owner: Piyush Ji | Greeneye Nursery, Jaipur | 22 March 2026 | Page 1: Plan view, Page 2: East elevation

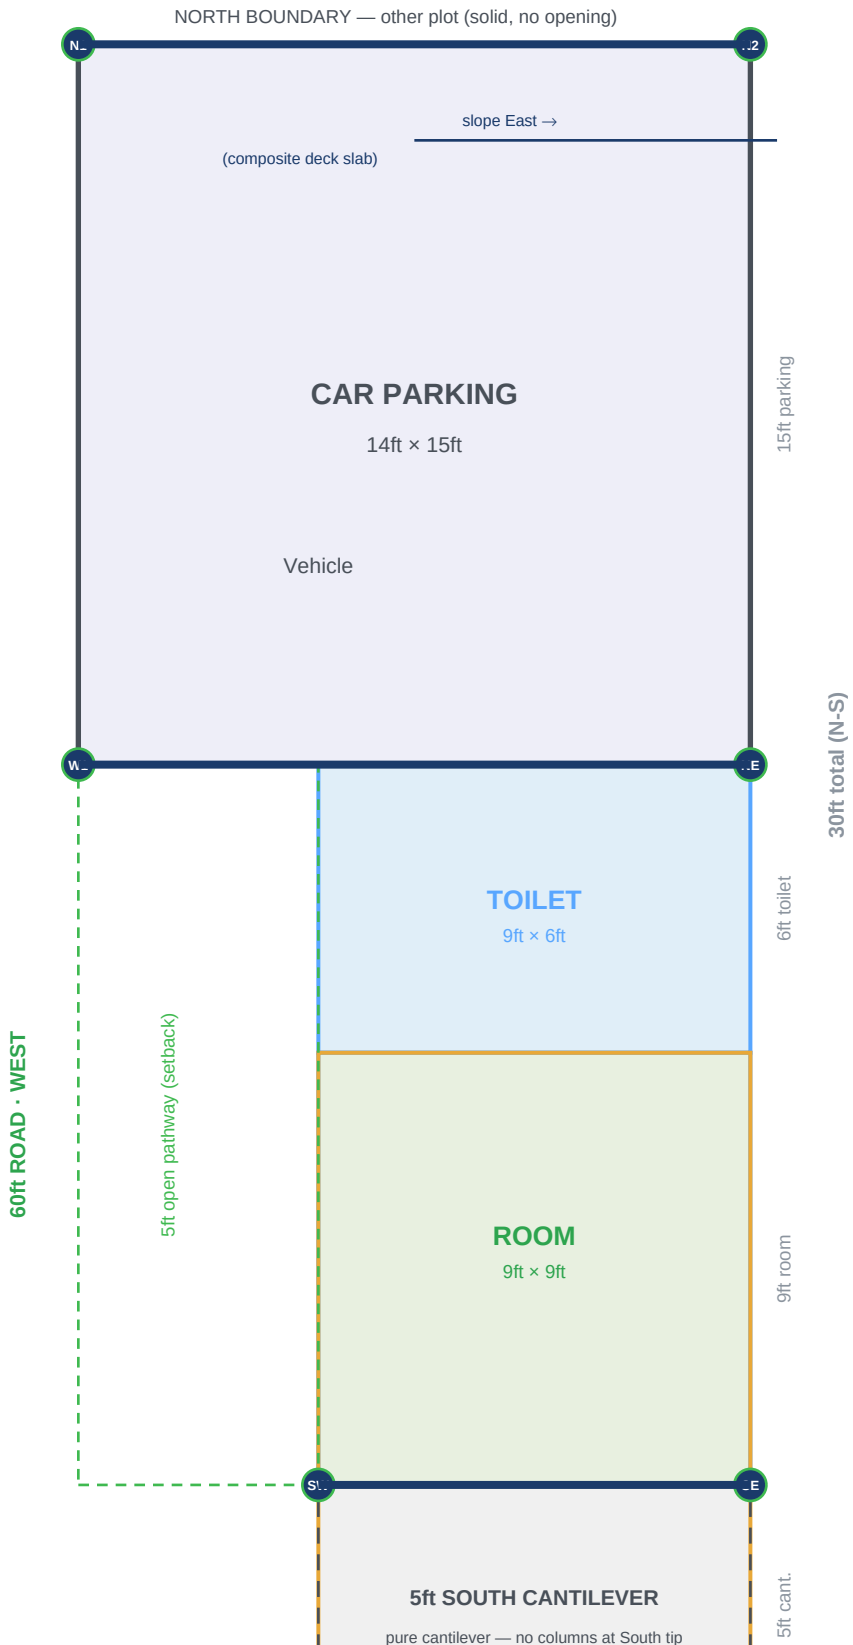

STRUCTURAL PLAN — top view (scale: 1ft = 18pt)



STRUCTURAL SPECIFICATION

COLUMNS

Total: 6 nos — 100×100×6 SHS
N1, N2: North boundary — parking NW & NE
W1: SW corner of parking (auto shutter)
NE: NE corner of toilet (N+E wall)
SW: West boundary at room S level
SE: East wall at room South level
Base: Base plate + anchor bolts, PCC footing
Height: ~10ft (max permitted)

BEAMS / SLAB

Primary: ISMB 150 @ N boundary, W1+NE, SW+SE
Purlins: MS Channel 100×50 @ ~5ft c/c (N-S)
Deck: Profiled GI metal deck (perm. form)
Topping: 75-100mm M20 concrete on deck

CANTILEVERS

South 5ft: Pure cantilever beyond SW+SE line
East 1ft: Overhang beyond East brick wall
West col.: N1, W1, SW — all on West boundary
East col.: N2, NE, SE — all on East wall

ROOF

Slope: East direction — 1:50 gradient
Drainage: Rainwater to nursery land (East)
Future: Tent/canopy on slab — no perm. floor

LEGEND

- 100×100 SHS column (6 total)
- ISMB 150 primary beam (E-W)
- Cantilever beam (no col. beyond)
- MS Channel 100×50 purlin (N-S)
- Composite deck slab footprint
- Cantilever zone (pure overhang)
- 5ft open pathway (setback)